


PLOT PLAN - LINEAR LOW DENSITY POLYETHYLENE (LLDPE) UNIT

Unit Layout at Grade | Highlighted: GA-1201A - HEXANE FEED PUMP (Area 1200)

BATTERY LIMIT

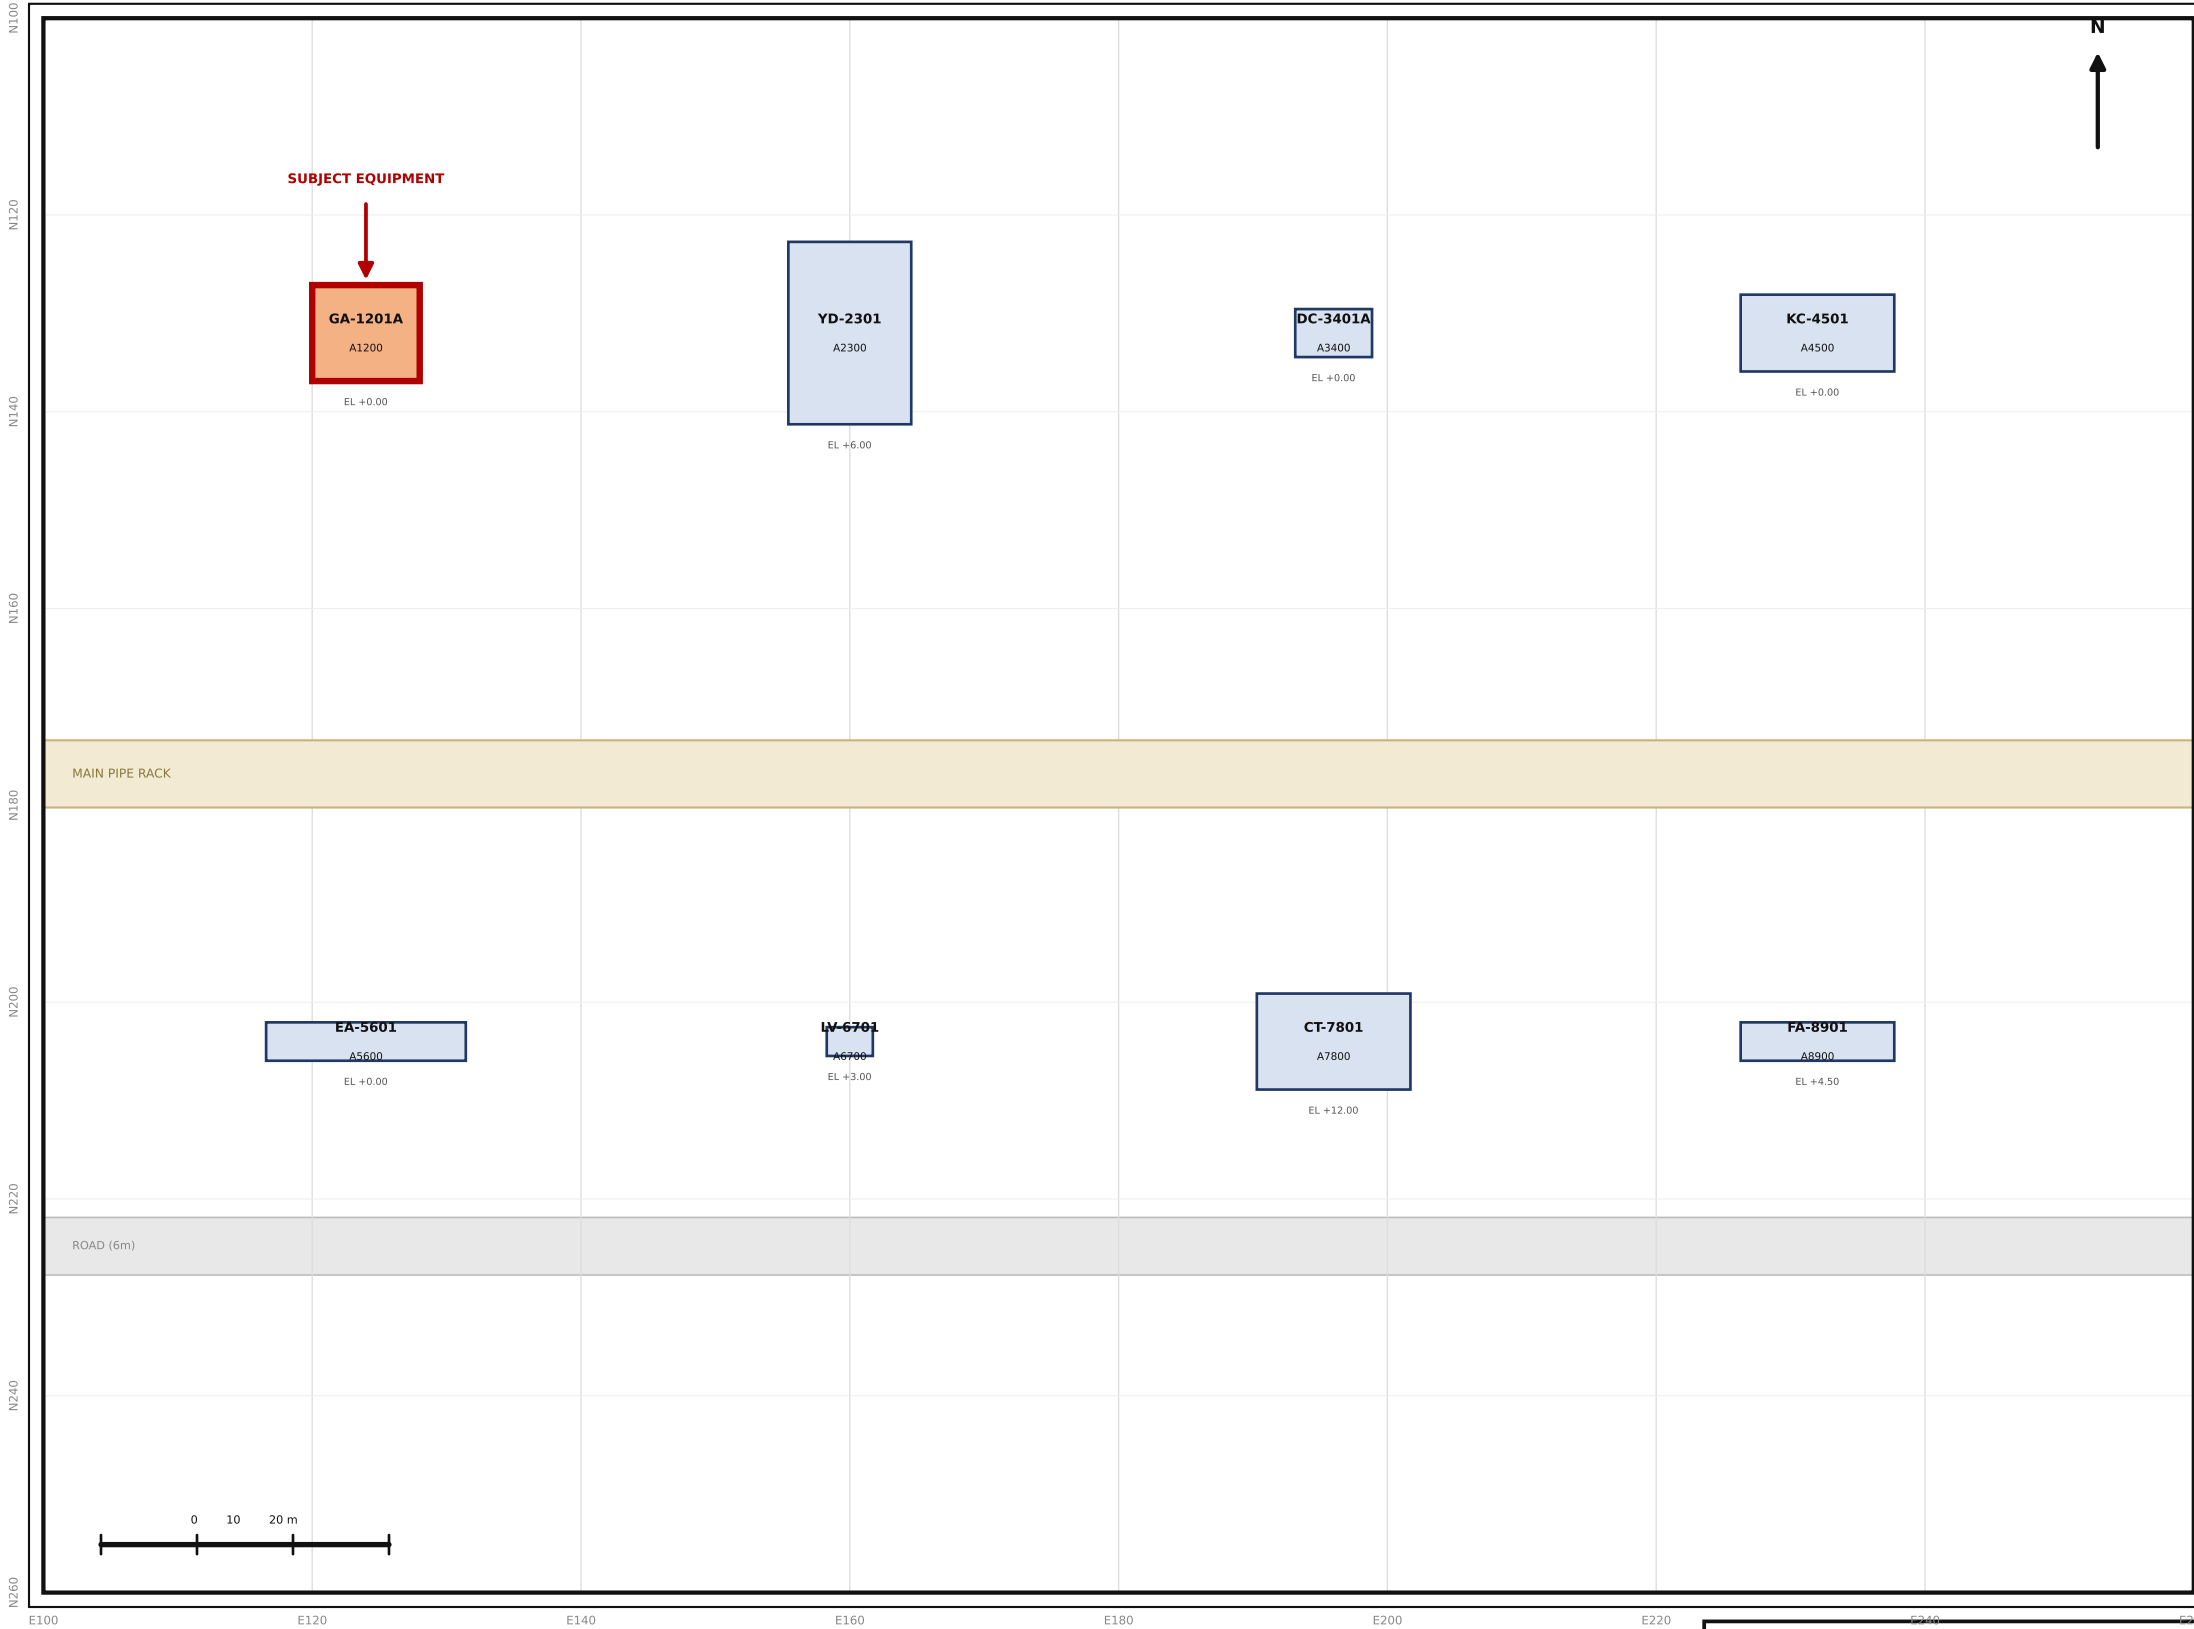

EQUIPMENT LOCATION DETAIL

TAG	GA-1201A
EQUIPMENT	HEXANE FEED PUMP
AREA	1200 - FEED PREPARATION & PURIFICATION
GRID REF	A-3
ELEVATION	EL +0.00
FUNCTIONAL LOC.	TJC-LLD-1200-01
FOOTPRINT	3.5 x 5.0 m (approx)

AREA LEGEND

	1200 - FEED PREPARATION & PURIFICATION
	2300 - POLYMER SEPARATION & DRYING
	3400 - CATALYST PREPARATION
	4500 - GAS RECOVERY & COMPRESSION
	5600 - SOLVENT RECOVERY SYSTEM
	6700 - PRODUCT SEPARATION
	7800 - COOLING WATER SYSTEM
	8900 - SOLVENT FRACTIONATION

NOTES:

- COORDINATES IN PLANT GRID (E/N), METRES.
- ELEVATIONS RELATIVE TO GRADE EL +0.00.
- EQUIPMENT SHOWN AT APPROX FOOTPRINT SCALE.
- REFER TO GA DRAWINGS FOR DETAIL.
- HAZARDOUS AREA CLASSIFICATION PER WPN-MAT-001.

REVISION HISTORY

REV	DESCRIPTION	BY	DATE
A	ISSUED FOR REVIEW	RS	15-05-2026
B	ISSUED FOR APPROVAL	RS	27-05-2026
D	ISSUED FOR CONSTRUCTION	RS	05-06-2026

This is sample data provided for CALIBER purposes only

TITLE:
PLOT PLAN / EQUIPMENT LOCATION

DWG No.
TJC-LLD-PP-GA-1201A

AREA 1200 - HEXANE FEED SYSTEM

REV: 0
SHEET 1 OF 1